


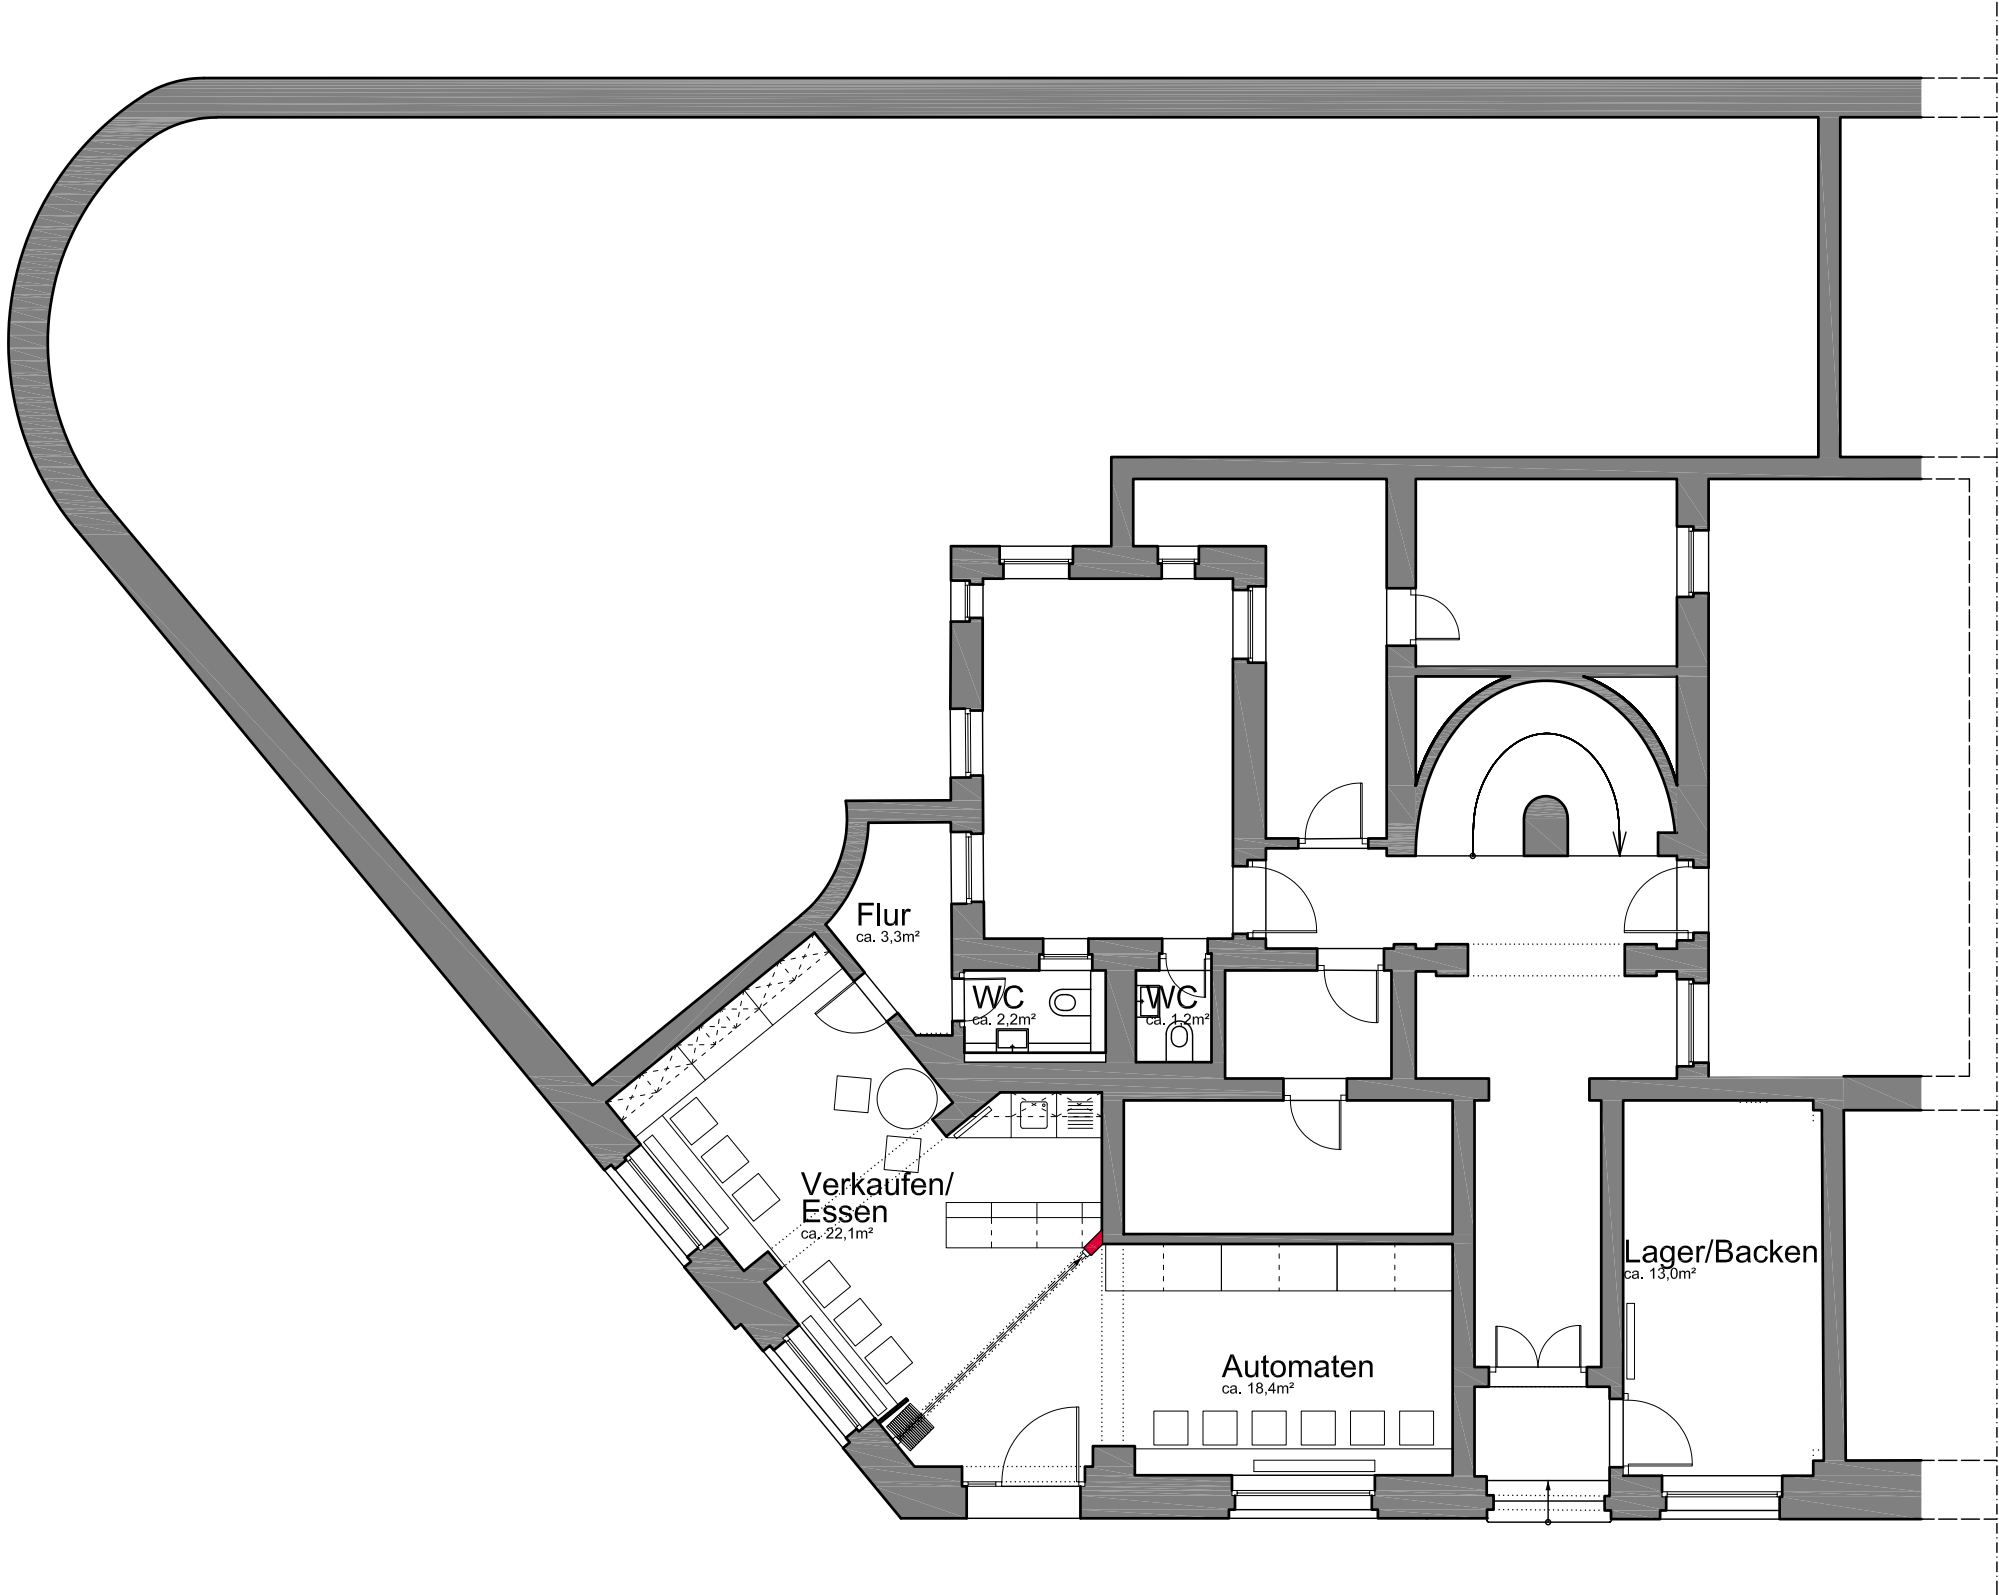

Planung:		Leonhard Satlow, Freier Architekt Schleißbergstr. 46, 01896 Ohorn Tel. 0162 - 825 02 54	Unterschrift:	VORHABEN:		Nutzungsänderung Gewerbeinheit zu Laden und Gastronomie Rudolf-Sendlig-Straße 3, 01814 Bad Schandau, Flurstücke 112 und 113	
Bauherr:		Elbsandstein Proviant & Quartier GmbH, Felix Zschoge Selbnersdorfer Straße 14, 01099 Dresden Tel. 0162 - 404 19 26	Unterschrift:	Datum:		08. September 2025	
				Maßstab:		1:100	
				Blattgröße:		42 x 29 ⁷ cm	
				Index:		-	
ALLE MASSE SIND EIGENVERANTWORTLICH AUF PLAN UND BAUSTELLE ZU ÜBERPRÜFEN! BEI GRÖßEREN ABWEICHUNGEN IST DER ENTWURFSVERFASSER UNVERZÜGLICH ZU INFORMIEREN. PROJEKTPÄNE DER BETEILIGTEN FACHPLANER SIND BEI DER AUSFÜHRUNG ZU BERÜCKSICHTIGEN.						Planung	
						LPH 4	
						Plannummer:	